2018-2023

CLARISE LUTIVA

ARCHITECTURAL PORTFOLIO

MANUAL WORKS

2018-2020

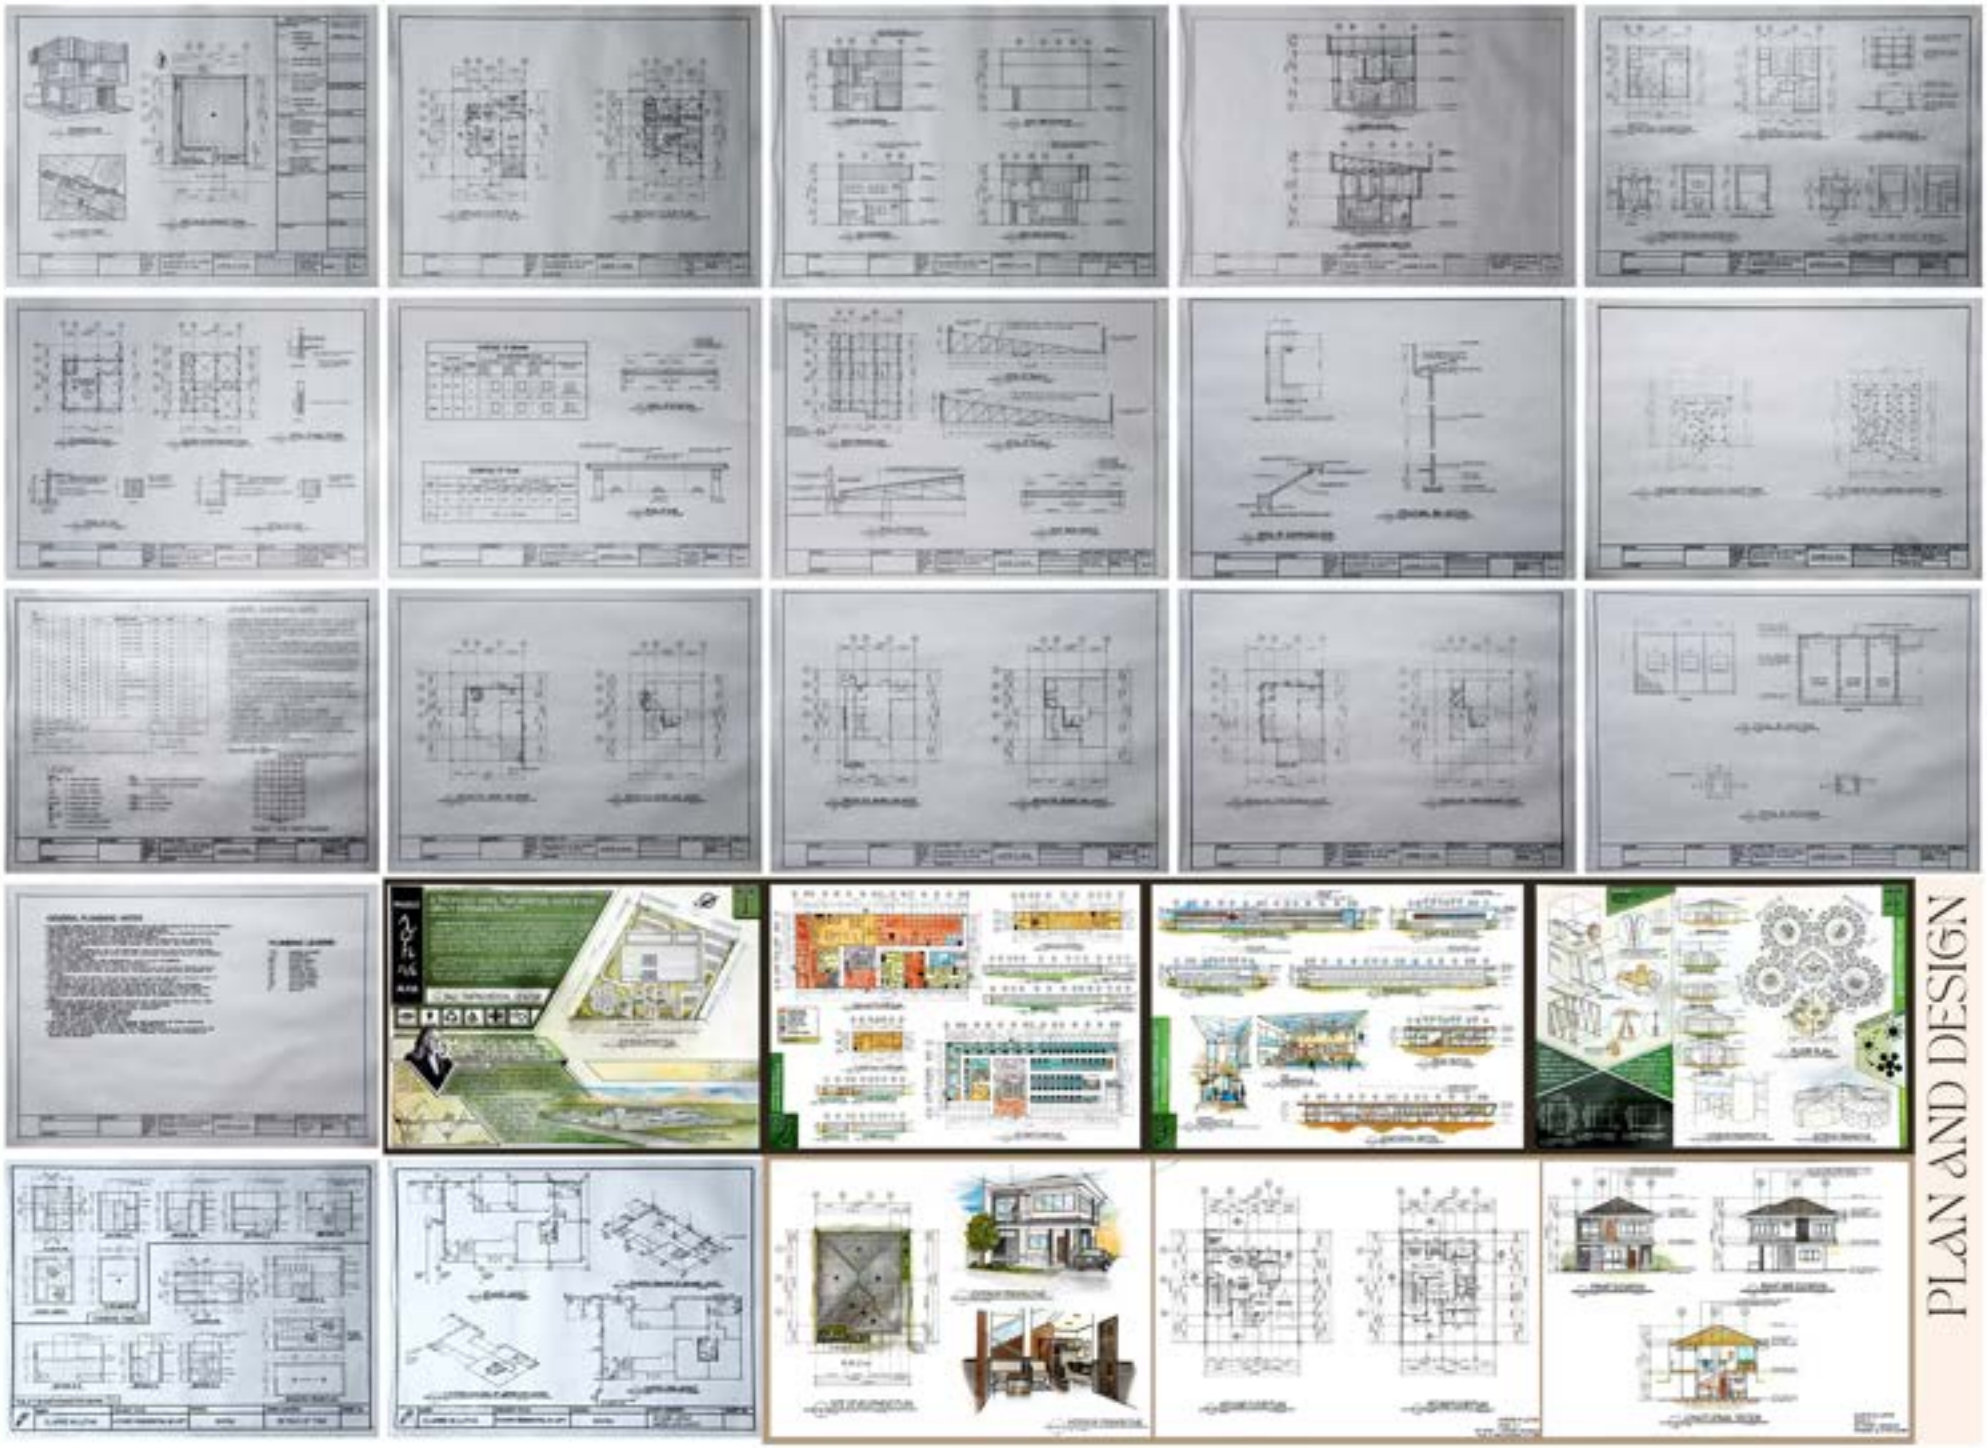

PLAN AND DESIGN

2020-2021

BEACH RESORT

SUKGISAN

PROJECT DURATION: JAN. 11-FEB. 18 2021

SITE DEVELOPMENT PLAN

PERSPECTIVE

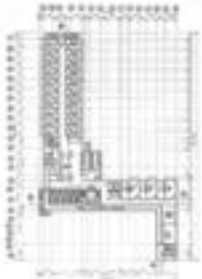

3-Star Hotel

MASTER DEVELOPMENT PLAN

Specialty Restaurant

TWO-BEDROOM RESORT VILLAS

TINY HOUSE

GLAMPING CABINS

Cabins

IKIGAI (生きがい)

LUTIVA, CLARISE M.
BSAR 3-1

MOODBOARD MAKING

Oriental Style Bedroom

PROJECT DURATION: JUNE 16-30 2021

SOFTWARES USED:

BACKYARD OASIS

SITE PLAN

SITE ELEVATION

PROJECT DURATION: MAY 18-25 2021

SOFTWARES USED:

SITE DEVELOPMENT PLAN

MERCADO DE BACOLOR

A MIXED USED COMMERCIAL DEVELOPMENT

Mercado de Bacolor is a proposed mixed-use commercial development project located in Bacolor, Pampanga, which seeks to commemorate the town's rich history through its architecture and public spaces. The complex will house a diverse range of shops, eateries, and entertainment venues, all crafted to deliver a distinctive and unforgettable experience. Drawing inspiration from the Spanish Colonial Architecture, the project's design pays homage to Bacolor's colonial roots while embracing its future. With the development set to breathe new life into the downtown area, Mercado de Bacolor is poised to emerge as a key attraction for visitors to Bacolor.

SITE ANALYSIS

VICINITY MAP

BACOLOR MUSEUM

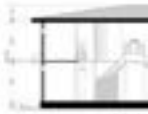

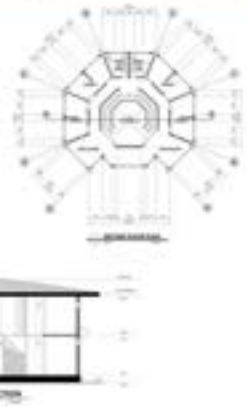

APARTMENTS

STUDIO-TYPE UNITS

INDOOR FOOD BAZAAR / RESTAURANT

COMMERCIAL BUILDING

PUBLIC PARK

MERCADO

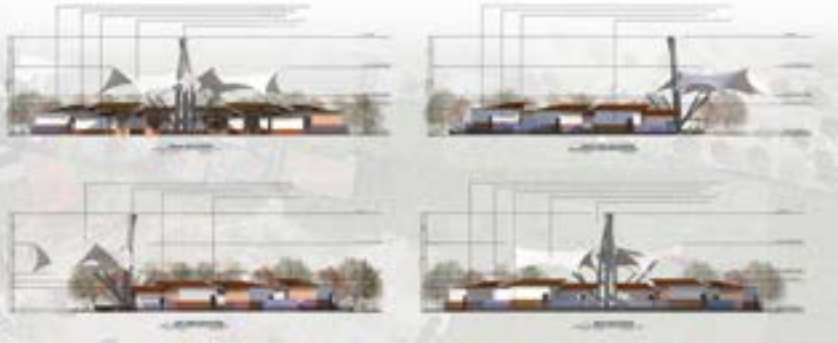

MULTIMODAL STREET DESIGN

Our final project for Architectural Design 7 centered around designing a multimodal street. Typical street designs usually prioritize cars over other modes of transportation, resulting in hazardous conditions for pedestrians, cyclists, and public transport users. The approach of multimodal street design aims to tackle this problem by identifying the requirements of all users. These requirements include wider sidewalks, dedicated bike lanes, and enhanced public transport infrastructure. The ultimate objective is to improve safety, accessibility, and encourage active transportation while reducing traffic congestion and enhancing air quality.

PROJECT DURATION: JAN. 17-28 2022
SOFTWARES USED:

2021-2022 (DSGN 415)

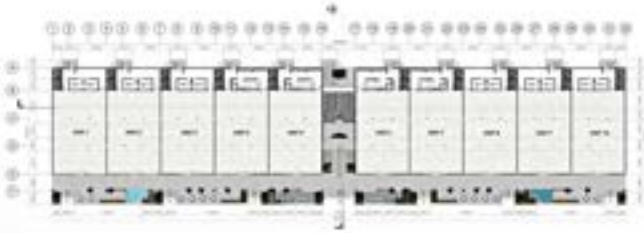

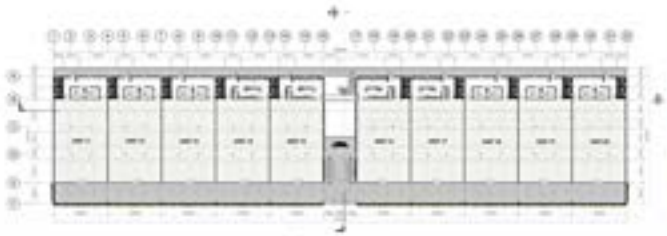

Strip Mall

PROJECT DURATION: MARCH 15-28 2022

SOFTWARES USED:

As we moved into Architectural Design B, our first task was to design a strip mall. For my project, I decided to design a linear single-corridor strip mall with incorporated greenery and foliage. Aside from various uses of plants and trees to simulate a natural and peaceful setting, the strip mall also features areas along the corridor with leisure spots and water features where people can relax and enjoy their surroundings. These features can attract more people to the mall, even those who may not be interested in shopping, but who are looking for a pleasant place to spend their time.

MEDICAL COMPACT VILLAGE

This building is part of a group project aimed at creating a development that caters to Medical Tourism. Named Project Buklod, the development comprises various features such as medical facilities, accommodations for medical tourists and medical personnel, and other relevant amenities. These buildings are designed with distinct concepts to reflect the site's locale - New Clark City's goal of constructing structures that emulate the Philippines' natural landmarks.

PROJECT BUKLOD

FACADE FORM CONCEPT

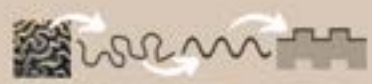

PLAN FORM CONCEPT

The building structure resembles a coral reef in form and fluidity. It can be expanded in the future by adding on to the two modules (a studio type unit for medical workers seeking privacy and a 2-bedroom unit for those seeking a companion and a less expensive option).

SITE FLOOR PLAN

MODULE 1:
STUDIO-TYPE

SECOND FLOOR PLAN

MODULE 1:
2-BEDROOM

THIRD FLOOR PLAN

FRONT ELEVATION

RIGHT SIDE ELEVATION

LEFT SIDE ELEVATION

REAR ELEVATION

LONGITUDINAL SECTION

PROJECT DURATION: MARCH 28-MAY 10, 2022

SOFTWARES USED:

CROSS SECTION

PROJECT BUKLOD is proposed to include a medical compact village to accommodate medical professionals and students from distant or foreign locations, ensuring their safety and availability to patients. The building's design is inspired by Tubbataha Reef and features a coral reef-like structure but geometric and cubic. The building is comprised of two standardized modules with suspended gardens on their roofs for leisure and relaxation. An outdoor reading area is also provided for the residents.

ZONE 2: 1-BEDROOM

1-BEDROOM (A)

1-BEDROOM (B)

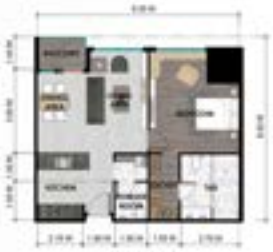

1-BEDROOM (C)

1-BEDROOM (D)

1-BEDROOM (E)

1-BEDROOM UNIT (A)

PROJECT DURATION: MAY 23- JUNE 25 2022

SOFTWARES USED:

ZONE 6: PENTHOUSE(1ST LEVEL)

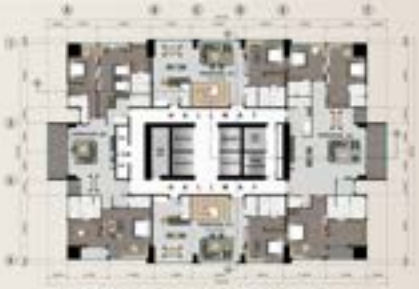

ZONE 6: PENTHOUSE(1ST LEVEL)

PENTHOUSE (A)

PENTHOUSE (B)

PENTHOUSE (C)
1ST LEVEL

PENTHOUSE (C)
2ND LEVEL

PENTHOUSE (B)

THE SKY PLAZA

For our last group project in Architectural Design 8, we had to design a high-rise condominium. I worked on designing two of our model units (five 1-bedroom and 3 penthouse prototypes). The one-bedroom spaces have minimalist and modern design, prioritizing storage and space maximization. The penthouses have spacious master bedrooms, en-suite bath-rooms, and private balconies. The penthouse embodies elegance and modernity.

In Architectural Design 10, we have been presented the opportunity to apply our accumulated learnings from previous semesters and formu-late a thesis. As a group, we have focused on developing a commercial project that aims to address ecological concerns, food insecurity, and provide fresh food sourcing options to metropolitan residents.

Our proposed mixed-use commercial project, named "EKÓS: A Proposed Complex Revitalizing Urban Commercial Framework through Agritecture," is located in the Central Business District of Quezon City and consists of several components, including the Ekós Towers, Agrimall, Agricentre, Apartments, and Ekós Park.

EKÓS

A Proposed Complex Revitalizing Urban Commercial Framework through Agritecture

PROJECT DURATION:
JAN. 28-APR. 29 2023

SOFTWARES USED:

THESIS MAGAZINE

3D Visualization

OTHER RENDERED PROJECTS

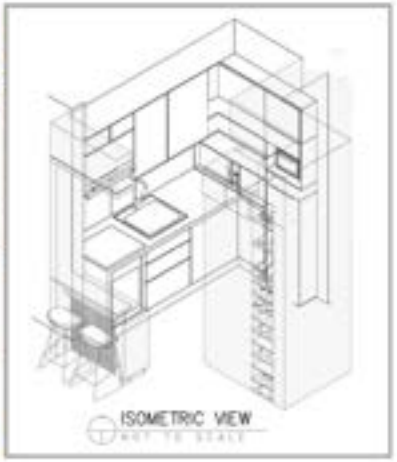

CONDO FIT-OUT

KITCHEN BLOW-UP DETAILS
FLOOR PLAN
SCALE 1: 30 MTS

SECTIONAL ELEV. (THRU-A)
SCALE

SECTIONAL ELEV. (THRU-B)
SCALE 1: 30 MTS

SOFTWARES USED:

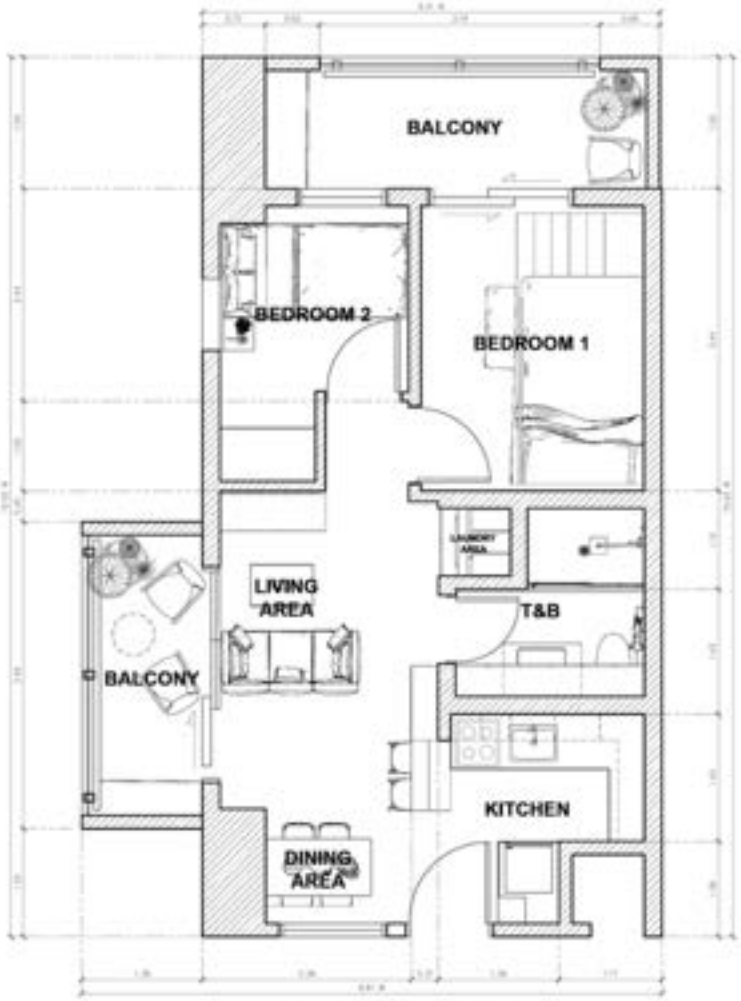

FLOOR PLAN
SCALE 1: 60 MTS

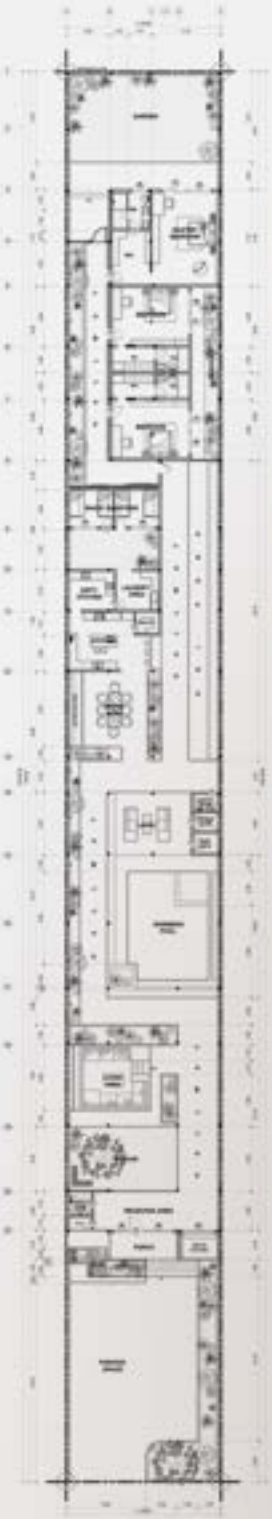

SITE FLOOR PLAN

SOFTWARES USED:

SOFTWARES USED: Ps

JAN-MAR 2024

RENDER WORKS

SOFTWARES USED:

RENDER WORKS

JAN-MAR 2024

MAUSOLEUM DESIGN

SOFTWARES USED:

GROUND FLOOR PLAN

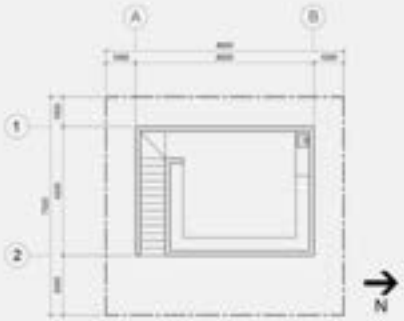

ROOF DECK PLAN

INTERIOR DESIGN *Exercise*

SOFTWARES USED:

JAN-AUGUST 2024

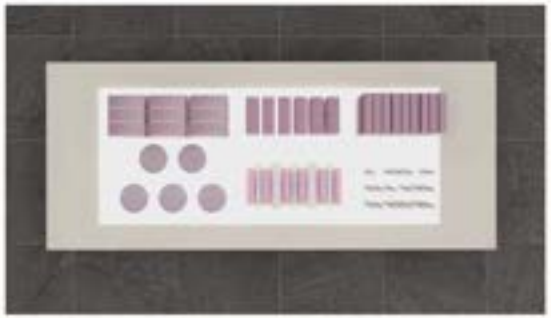

Expo Booth Design

SOFTWARES USED:

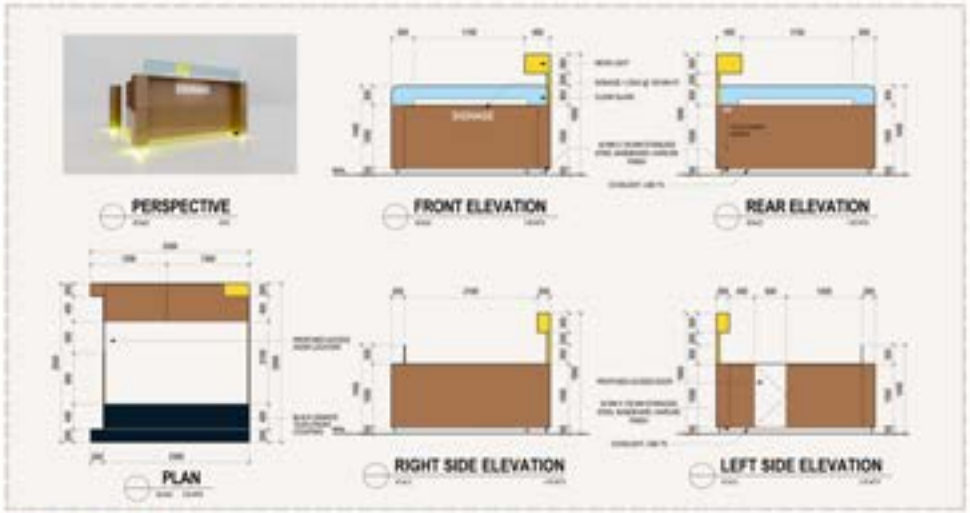

DESIGN AND RENDER WORKS

POLYHOME
Modular House

RENDERING WORKS

SOFTWARES USED:

FLOOR PLAN

FRONT ELEVATION

RIGHT SIDE ELEVATION

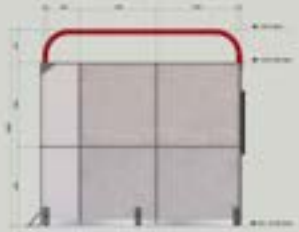
LEFT SIDE ELEVATION

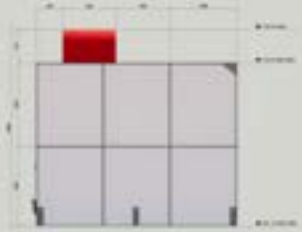
REAR ELEVATION

Expo Booth

PROJECT DURATION: JULY -SEPT. 2024

SOFTWARES USED:

coffee shop | 3d modelling, rendering & cad drafting

SOFTWARES USED:

3 A-01 FLOOR PLAN

4 A-01 FRONT ELEVATION

5 A-01 RIGHT SIDE ELEVATION

1 A-02 LEFT SIDE ELEVATION

2 A-02 REAR ELEVATION

3 A-02 SECTION THRU "A-A"

4 A-02 SECTION THRU "B-B"

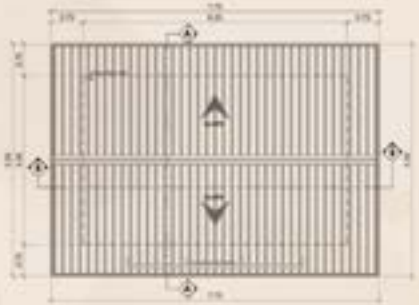

1 A-03 ROOF PLAN

2 A-03 REFLECTED CEILING PLAN

3 A-03 SCHEDULE OF DOORS AND WINDOWS

GROUND FLOOR PLAN

SECOND FLOOR PLAN

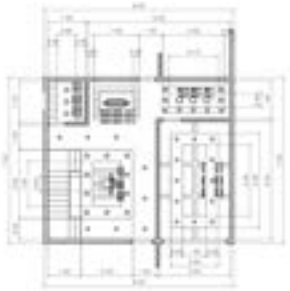

GROUND FLOOR CEILING PLAN

SECOND FLOOR CEILING PLAN

GROUND FLOOR PATTERN LAYOUT

SECOND FLOOR PATTERN LAYOUT

FRONT ELEVATION

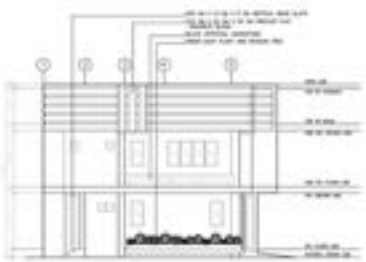

RIGHT SIDE ELEVATION

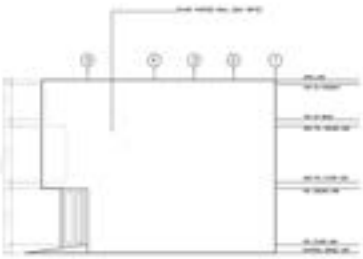

LEFT SIDE ELEVATION

REAR ELEVATION

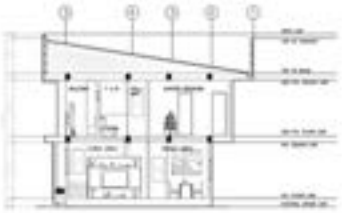

CROSS SECTION

LONGITUDINAL SECTION

GROUND FLOOR WATER LINE LAYOUT

SECOND FLOOR WATER LINE LAYOUT

ISOMETRIC LAYOUT

CAD
DRAFTING

GROUND FLOOR SEWER LINE LAYOUT

SECOND FLOOR SEWER LINE LAYOUT

ISOMETRIC LAYOUT

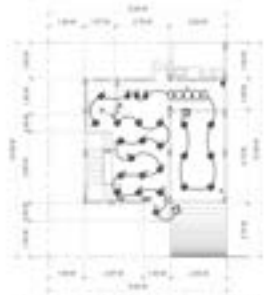

GROUND FLOOR LIGHTING LAYOUT

SECOND FLOOR LIGHTING LAYOUT

GROUND FLOOR POWER LAYOUT

SECOND FLOOR POWER LAYOUT

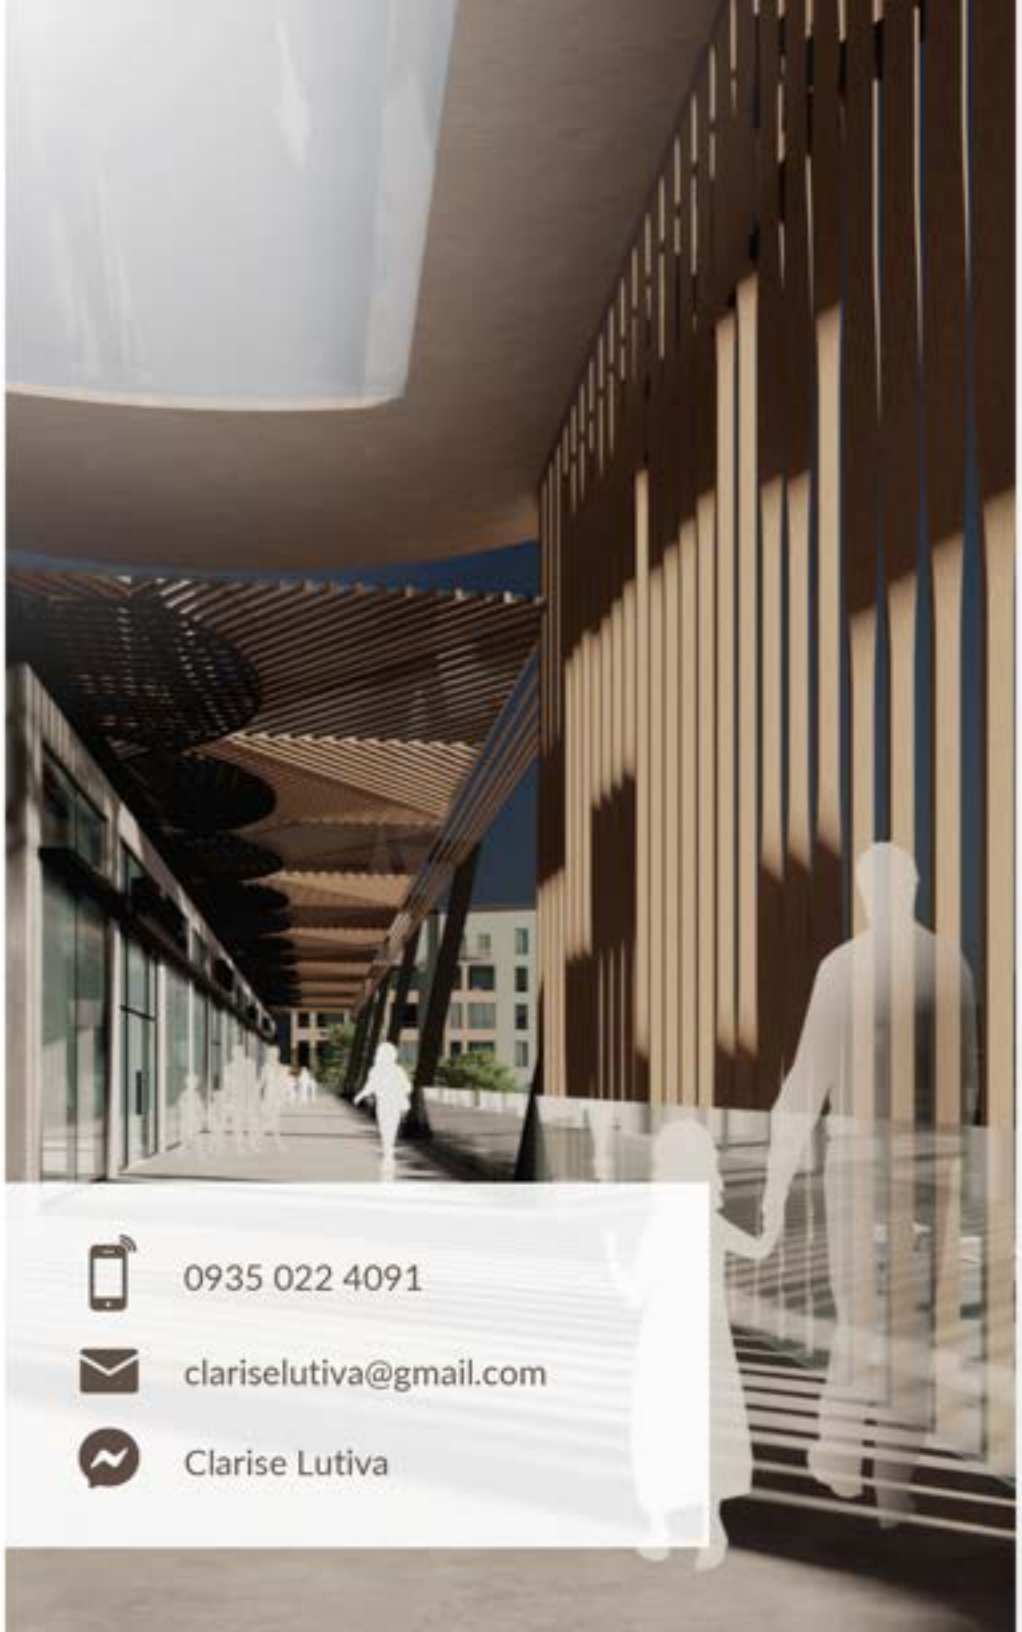

0935 022 4091

clariselutiva@gmail.com

Clarise Lutiva

CLARISE LUTIVA

Clarise Lutiva is a graduate of Don Honorio Ventura State University with a Bachelor of Science in Architecture. Through both academic training and professional experience, she has developed skills in architectural drafting, rendering, scale modeling, visualization, and layout. She has been involved in the design and preparation of architectural plans and models, gaining practical experience in applying design concepts to real-world projects. She is continuously learning and working to improve her capabilities, with the goal of becoming a registered and licensed architect. She remains committed to contributing meaningfully to the field of architecture while growing through each opportunity and challenge.

C.M.LUTIVA